Zyra kadastrale komunale / Ferizaj

Zona kadastrale / Katastarska zona: Ferizaj

Lloji i njësisë kadastrale / Vrsta katastarske jedinice : Objekt

Skica e matjes

Emri i investitorit Morea

Shkalla e zvoglimit / Razmera plana 1: 250

Lloji i punes Analizë e sip të garazhave

Analiza e sipërfaqeve të garazhave				
Pronari	Kultura	Llamela	Sipërfaqia	
Gazi	Garazhë	LID	19.53	m²
Gazi	Garazhë	LID	28.83	m²
Gazi	Garazhë	LID	18.29	m²
Gazi	Garazhë	LID	21.08	m²
Gazi	Garazhë	LID	17.83	m²
Gazi	Garazhë	LID	17.82	m²
Gazi	Garazhë	LID	28.83	m²
Gazi	Garazhë	LID	0.11	m²
Gazi	Garazhë	LID	1.55	m²
Gazi	Garazhë	LID	2.16	m²
Gazi	Garazhë	LID	3.04	m²
Gazi	Garazhë	LID	8.22	m²
Gazi	Hapsirë Komunikuse	LID	122.43	m²
Gazi	Garazhë	LIE	27.06	m²
Gazi	Garazhë	LIE	26.03	m²
Gazi	Garazhë	LIE	5.11	m²
Gazi	Garazhë	LIE	19.34	m²
Gazi	Garazhë	LIE	27.59	m²
Gazi	Garazhë	LIE	33.79	m²
Gazi	Garazhë	LIE	22.16	m²
Gazi	Garazhë	LIE	20.77	m²
Gazi	Garazhë	LIE	17.74	m²
Gazi	Garazhë	LIE	18.99	m²
Gazi	Garazhë	LIE	28.83	m²
Gazi	Garazhë	LIE	10.32	m²
Gazi	Garazhë	LIE	14.22	m²
Gazi	Hapsirë Komunikuse	LIE	214.11	m²
Gazi	Hapsirë Komunikuse	LIE	0.12	m²
Gazi	Hapsirë Komunikuse	Oborr	30.31	m²
Gazi	Rampa	Oborr	40.51	m²
		Gjithsej	846.72	m²

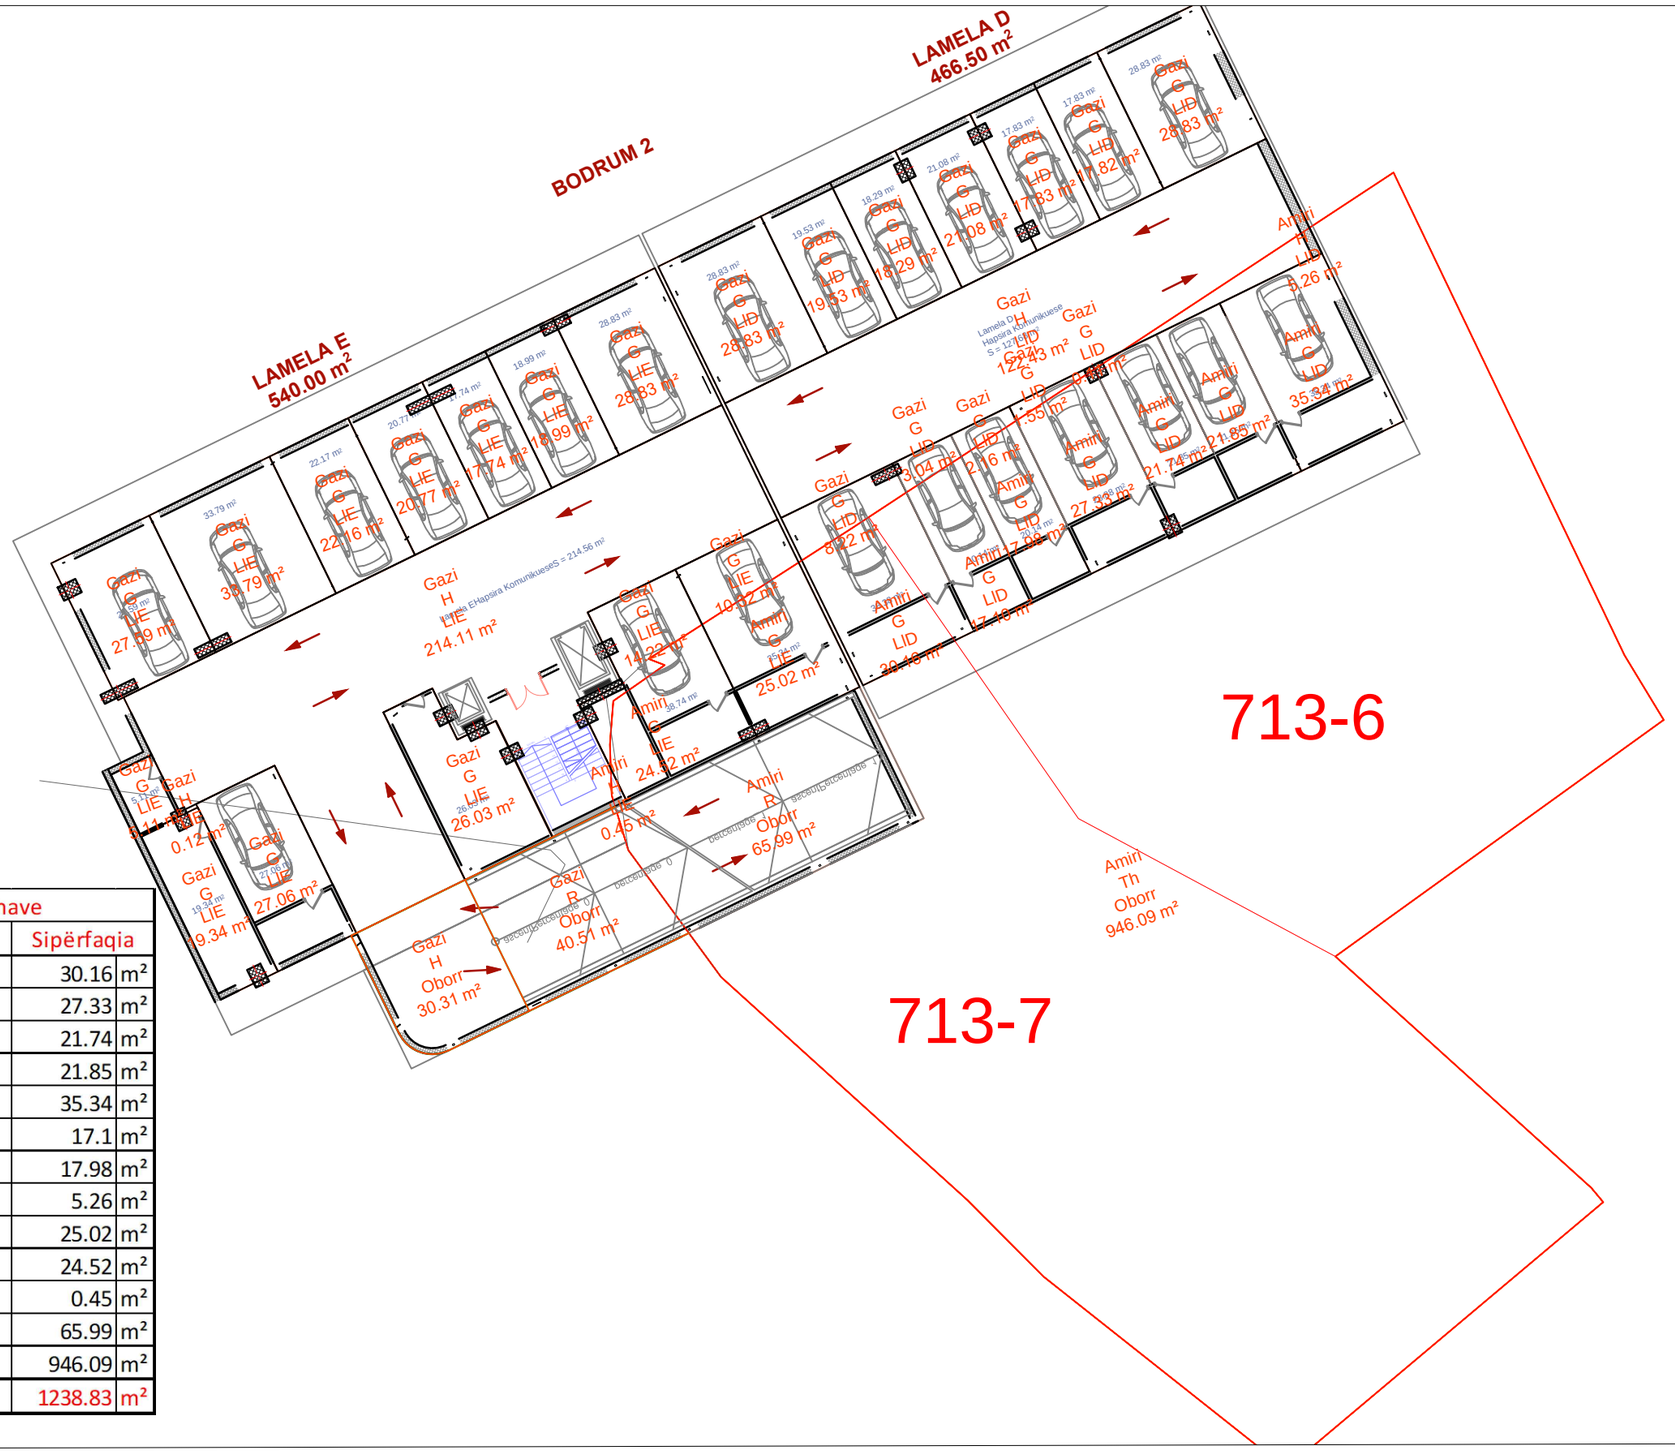

Analiza e sipërfaqeve të garazhave				
Pronari	Kultura	Llamela	Sipërfaqia	
Amiri	Garazhë	LID	30.16	m²
Amiri	Garazhë	LID	27.33	m²
Amiri	Garazhë	LID	21.74	m²
Amiri	Garazhë	LID	21.85	m²
Amiri	Garazhë	LID	35.34	m²
Amiri	Garazhë	LID	17.1	m²
Amiri	Garazhë	LID	17.98	m²
Amiri	Hapsirë Komunikuse	LID	5.26	m²
Amiri	Garazhë	LIE	25.02	m²
Amiri	Garazhë	LIE	24.52	m²
Amiri	Hapsirë Komunikuse	LIE	0.45	m²
Amiri	Rampa	Oborr	65.99	m²
Amiri	Pa ndërtim	Oborr	946.09	m²
		Gjithsej	1238.83	m²

Rilevoi / Snimio: ing.LIRIDON SEJDIU
(emri dhe mbiemri i gjeodetit/kompanisë/ ime i prezime geodeta/ kompanije)

Nr.i tel.: 049-535-250

V.V.

Nënshkrimi / Potpis: _____

Data e rilevimit / Datum snimanja: 18.04.2022

Rilevoi / Snimio: ing. SEAD PRUSHI
(emri dhe mbiemri i gjeodetit/kompanisë/ ime i prezime geodeta/ kompanije)

Nr.i tel.: 044-791-828

Nënshkrimi / Potpis: _____

Data e rilevimit / Datum snimanja: _____