Zyra kadastrale komunale / Opštinska katastarska kancelarija: Ferizaj

Zona kadastrale / Katastarska zona: FERIZAJ

Lloji i njësisë kadastrale / Vrsta katastarske jedinice : Situacion objektit

Nr. i njësisë kadastrale / Br. katastarske jedinice : 3431-0

Numri i lëndës / Broj predmeta:

Shkalla e zvoglimit / Razmera plana : 1:250

Republika e Kosovës

Republika Kosova-Republic of Kosova

Qeveria -Vlada-Government

Ministria e Mjedisit dhe Planifikimit Hapësinor /Ministarstvo Sredine i Prostornog Planiranja/Ministry of Environment and Spatial Planning

AGJENCIA KADASTRALE E KOSOVËS/ KATASTARSKA AGECIJA KOSOVA/ KOSOVA CADASTRAL AGENCY

Koordinatat e Katit 5 te ekzekutuar

Nr	Y	X	H	Kodi	Përshkrimi	Burimi
110	7512008.932	4692333.172	636.739	KAATI-5	Shtëpi-Ndërtesë	PM
111	7511998.947	4692318.028	636.739	KAATI-5	Shtëpi-Ndërtesë	PM
112	7511986.552	4692326.155	636.739	KAATI-5	Shtëpi-Ndërtesë	PM
113	7511987.339	4692327.365	636.739	KAATI-5	Shtëpi-Ndërtesë	PM
114	7511985.097	4692328.807	636.739	KAATI-5	Shtëpi-Ndërtesë	PM
115	7511983.297	4692327.389	636.739	KAATI-5	Shtëpi-Ndërtesë	PM
116	7511983.559	4692327.051	636.739	KAATI-5	Shtëpi-Ndërtesë	PM
117	7511974.875	4692320.054	636.739	KAATI-5	Shtëpi-Ndërtesë	PM
118	7511964.979	4692332.410	636.739	KAATI-5	Shtëpi-Ndërtesë	PM
119	7511985.293	4692348.734	636.739	KAATI-5	Shtëpi-Ndërtesë	PM
109	7511989.341	4692345.463	636.739	K5-FS1	Pikë Poligonale	PM

Koordinatat e katit karakteristik të projektuar

Nr	Y	X	H	Kodi	Përshkrimi	Burimi
1	7511987.361	4692327.353	-	40	Shtëpi-Ndërtesë	PM
2	7511985.104	4692328.839	-	40	Shtëpi-Ndërtesë	PM
3	7511983.296	4692327.387	-	40	Shtëpi-Ndërtesë	PM
4	7511983.546	4692327.076	-	40	Shtëpi-Ndërtesë	PM
5	7511974.853	4692320.093	-	40	Shtëpi-Ndërtesë	PM
6	7511964.959	4692332.412	-	40	Shtëpi-Ndërtesë	PM
7	7511985.269	4692348.725	-	40	Shtëpi-Ndërtesë	PM
8	7512008.906	4692333.162	-	40	Shtëpi-Ndërtesë	PM
9	7511998.899	4692317.963	-	40	Shtëpi-Ndërtesë	PM
10	7511986.537	4692326.100	-	40	Shtëpi-Ndërtesë	PM

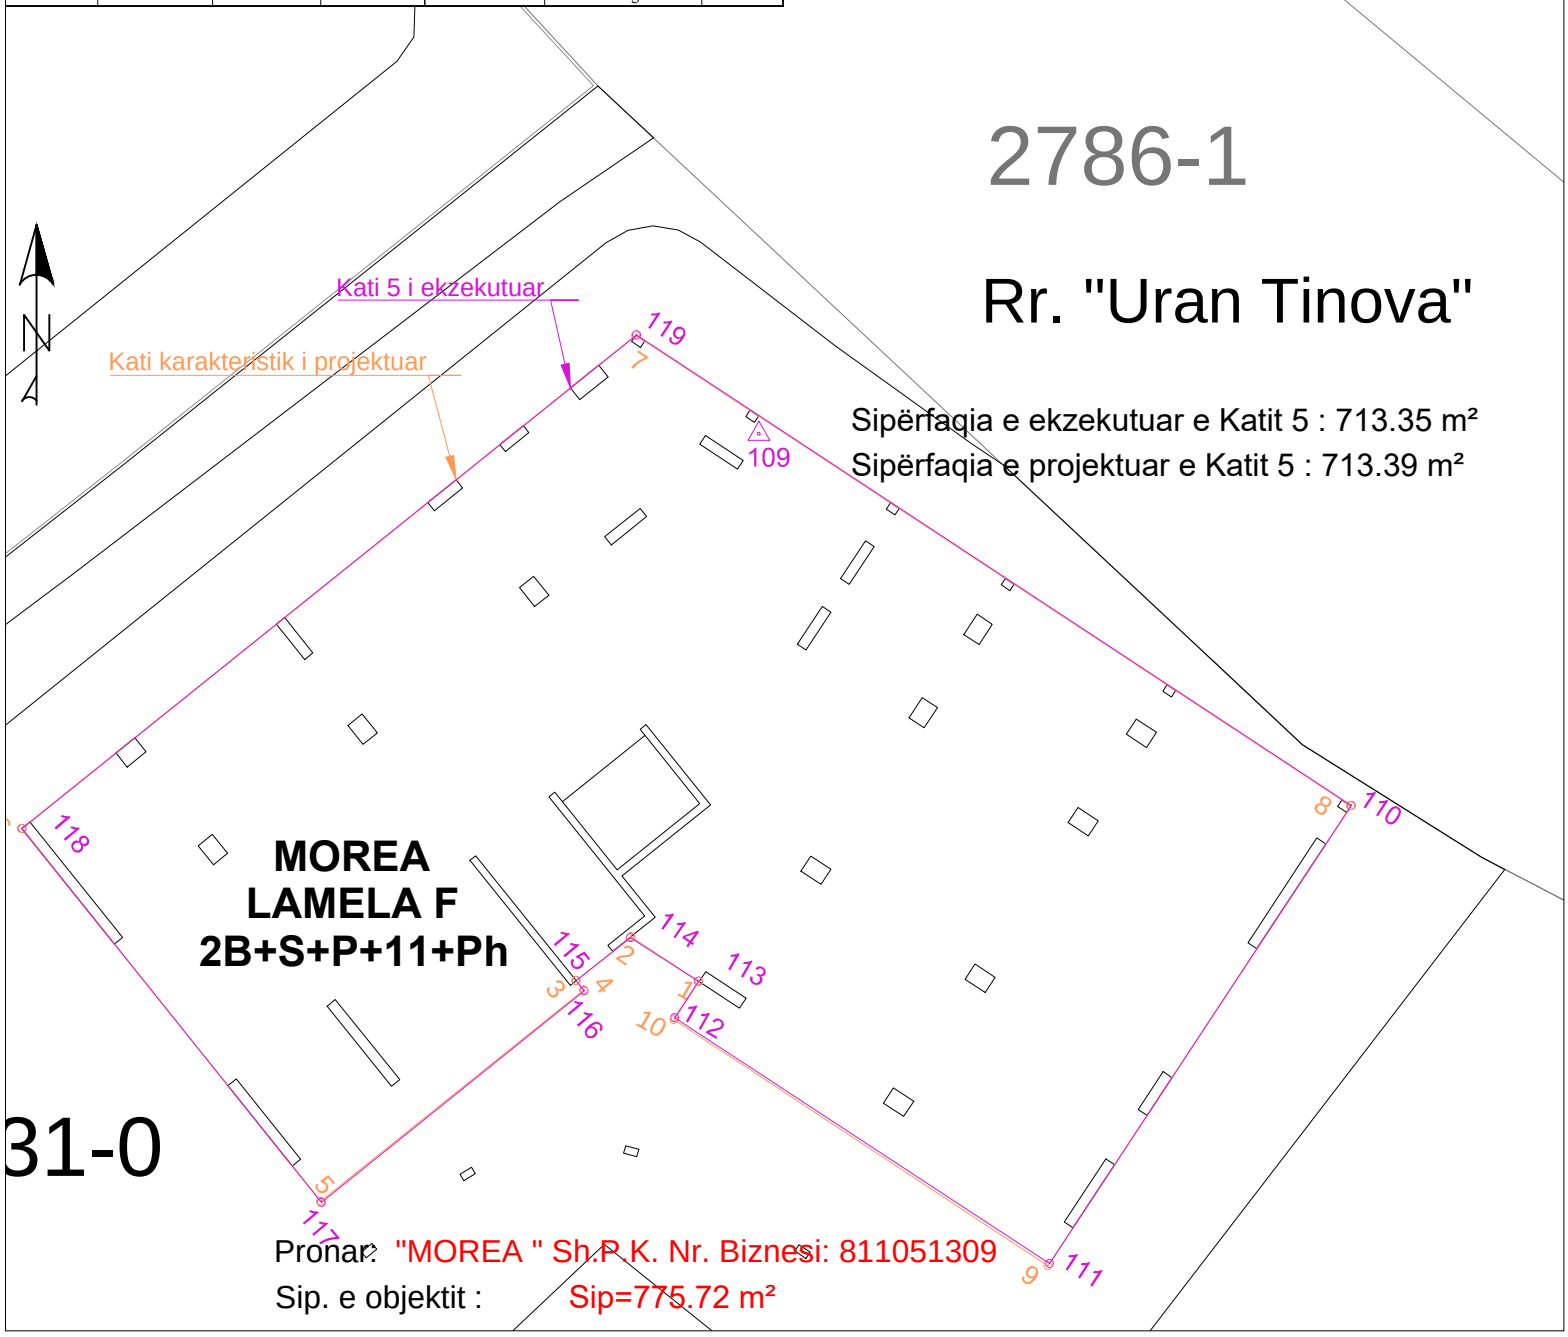

Rilevoi / Snimio: Liridon Sejdiu

(emri dhe mbiemri i gjeodetit/kompanisë/ ime i prezime geodeta/ kompanije)

Etazha: Kati 5

Nr. i licencës / Br. licence: 140

V.V.

Nënshkrimi / Potpis:

Nënshkrimi / Potpis:

Data e rilevimit / Datum snimanja: 18.05.2023

Data e aprovimit / Datum usvajanja: